


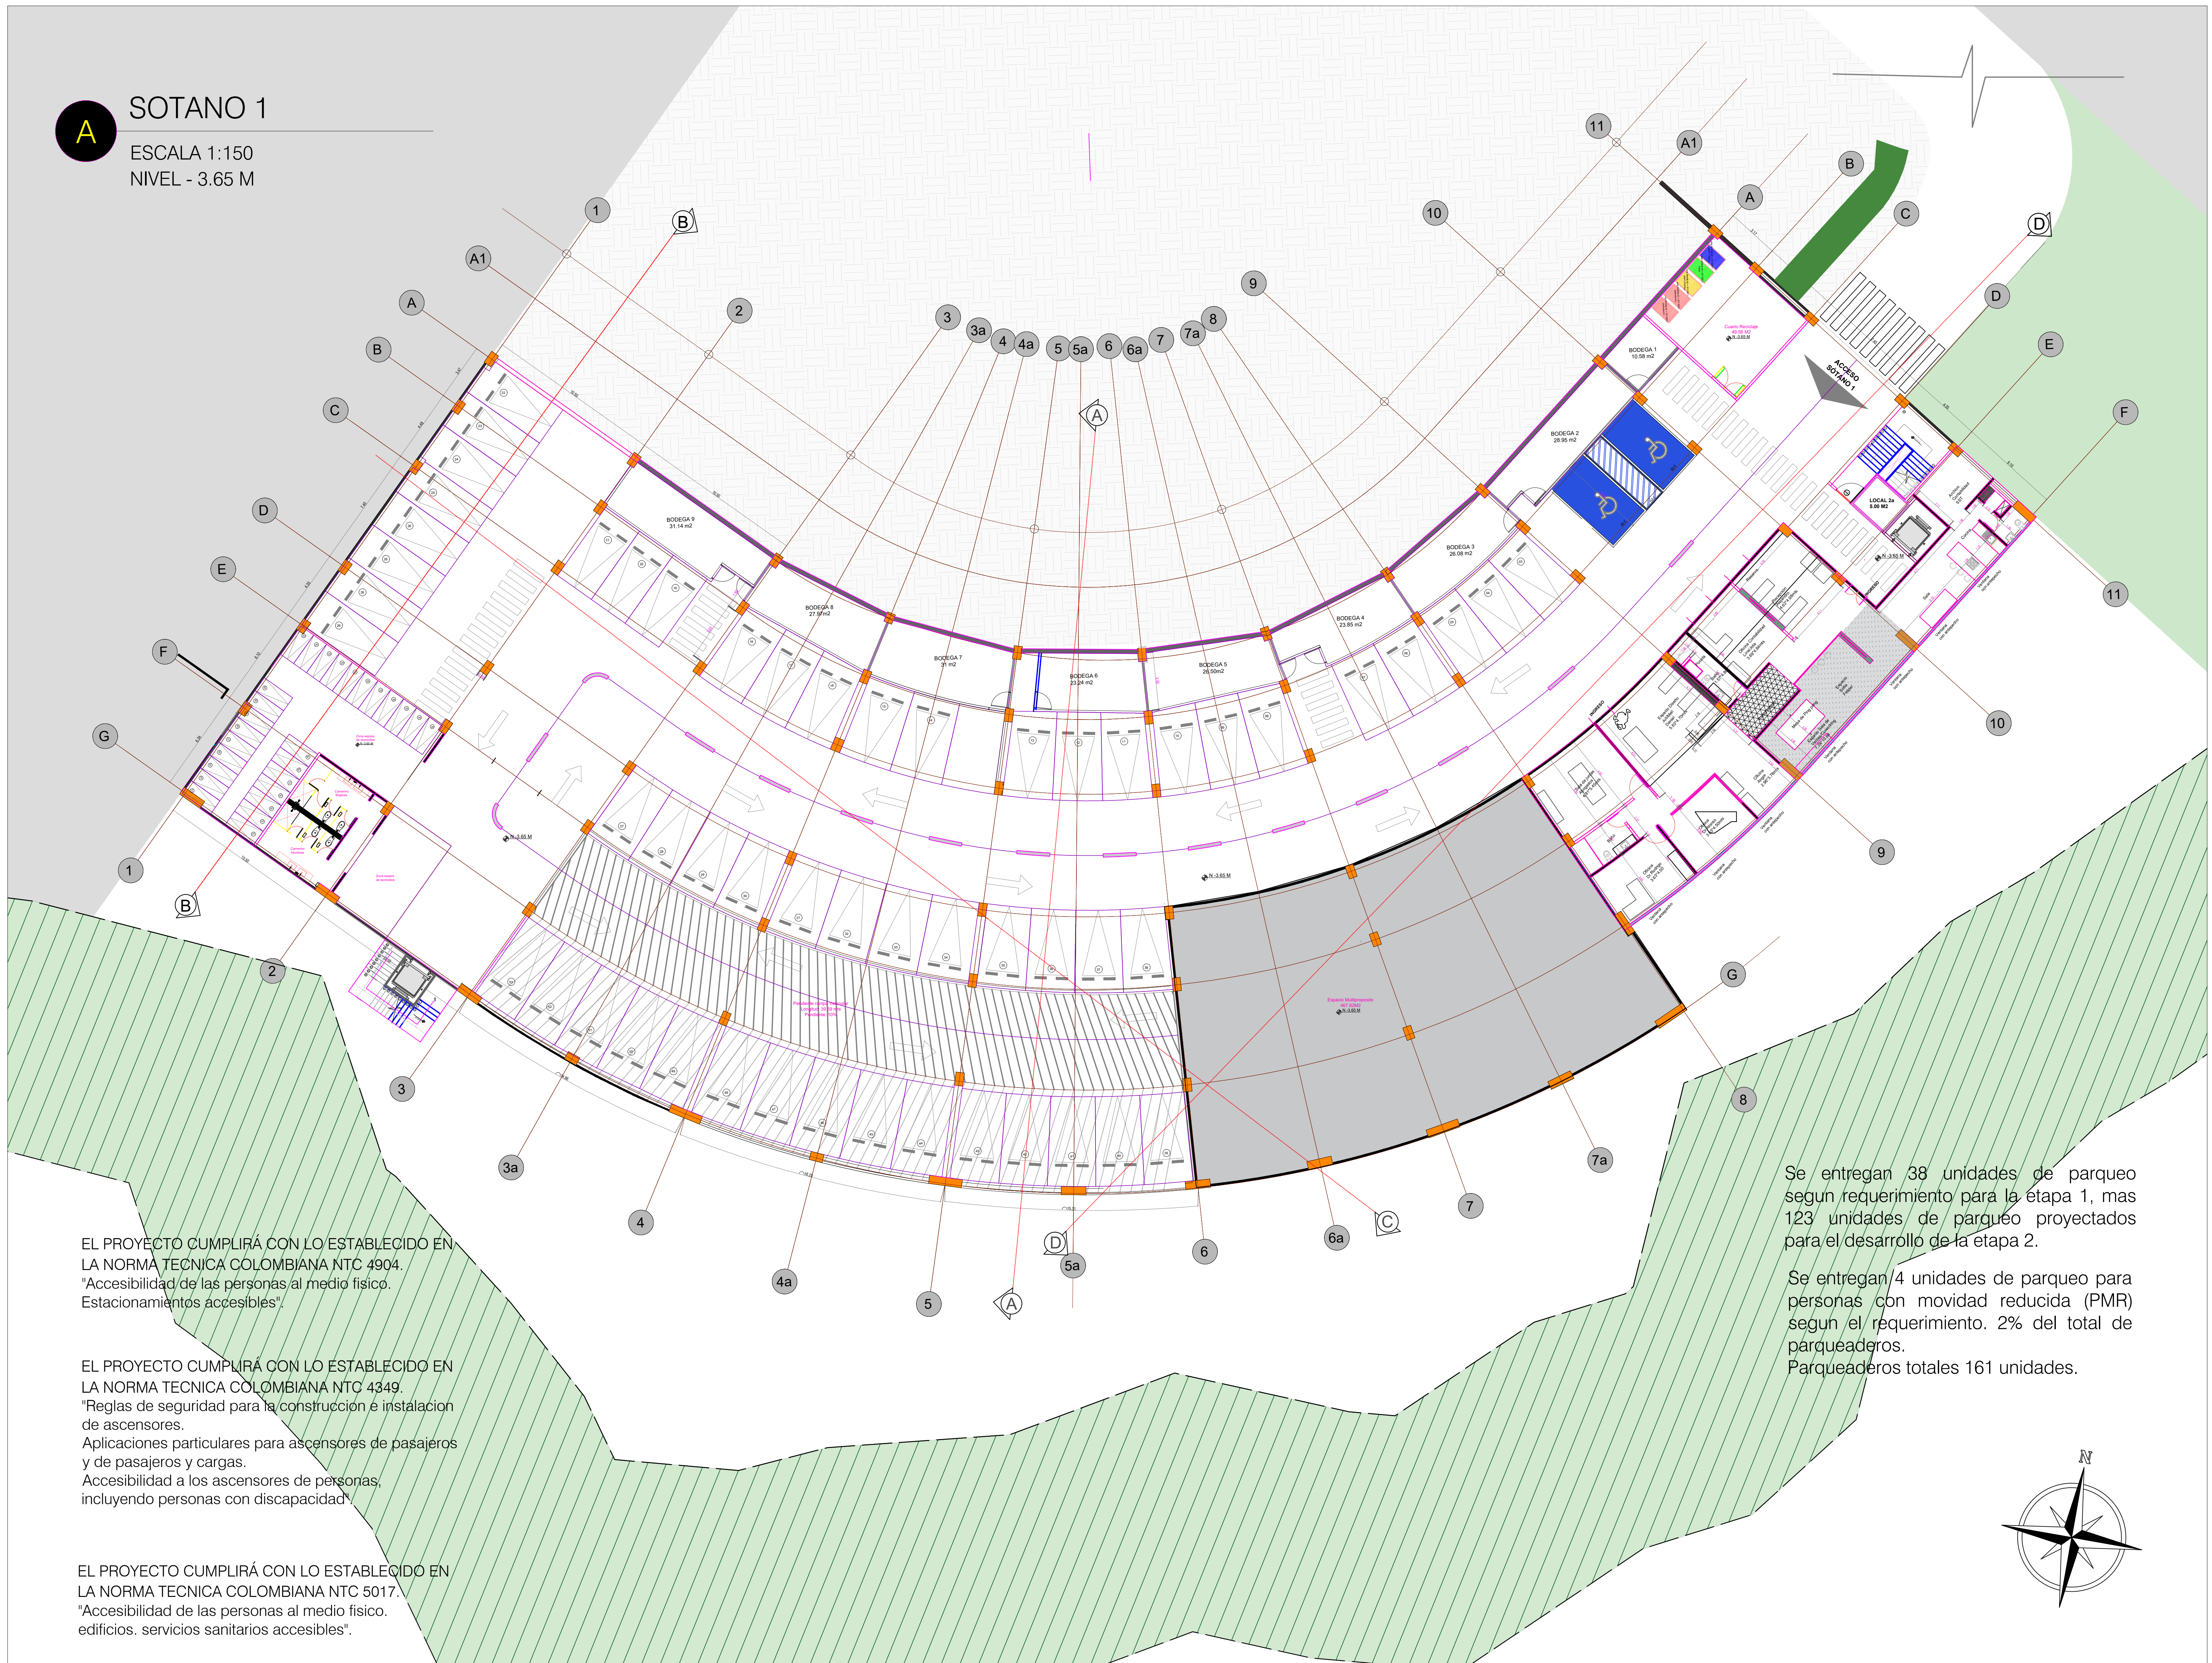

SOTANO 1

ESCALA 1:150
NIVEL - 3.65 M



EL PROYECTO CUMPLIRÁ CON LO ESTABLECIDO EN LA NORMA TECNICA COLOMBIANA NTC 4904.
"Accesibilidad de las personas al medio físico.
Estacionamientos accesibles".

EL PROYECTO CUMPLIRÁ CON LO ESTABLECIDO EN LA NORMA TECNICA COLOMBIANA NTC 4349.
"Reglas de seguridad para la construcción e instalación de ascensores.
Aplicaciones particulares para ascensores de pasajeros y de pasajeros y cargas.
Accesibilidad a los ascensores de personas, incluyendo personas con discapacidad".

EL PROYECTO CUMPLIRÁ CON LO ESTABLECIDO EN LA NORMA TECNICA COLOMBIANA NTC 5017.
"Accesibilidad de las personas al medio físico.
edificios, servicios sanitarios accesibles".

Se entregan 38 unidades de parqueo segun requerimiento para la etapa 1, mas 123 unidades de parqueo proyectados para el desarrollo de la etapa 2.

Se entregan 4 unidades de parqueo para personas con movilidad reducida (PMR) segun el requerimiento. 2% del total de parqueaderos.
Parqueaderos totales 161 unidades.

PLANO 04 20

BAHÍA GUACAMAYAS
PROYECTO COMERCIAL

PROYECTO:

BAHÍA GUACAMAYAS
"UN DESARROLLO EXCEPCIONAL"

DISEÑO Y CONSTRUYE:

Numancia

DEPARTAMENTO DE RISARALDA

DIRECCIÓN:
VEREDA FONDA CENTRAL LOTE 3.
SECTOR CERRITOS, PEREIRA

DR. RODRIGO OCAMPO OSSA
C.C. 19101474
GERENTE DEL PROYECTO

JULIAN DAVID ZAPATA
T.P. A17862017-1090149794
DIRECTOR DE OBRA

CONTENIDO:
Planta Arquitectónica N.E.-3.65mts
Sótano 1.

TRAMITE:
Licencia de Construcción
Modificación

EQUIPO DE TRABAJO

MELISA GIRALDO OSORIO
ARQUITECTA
M.P. A178212020-1088030422

NOMBRE DEL ARCHIVO:
16072025_Plantas Bahía Guacamayas.dwg

FECHA:
Mod_Junio_2025

ESCALA:
INDICADAS

VERSIÓN DEL ARCHIVO | 02

ANOTACIONES:
Mod_Junio_2025 - ANOTACIONES

Nota:
El contenido de este documento es confidencial y dirigido únicamente a su destinatario (s) queda expresamente prohibida su reproducción y divulgación de manera total o parcial sin autorización. Todos los derechos reservados.

BAHÍA GUACAMAYAS
PROYECTO COMERCIAL

PLANO 04 20