


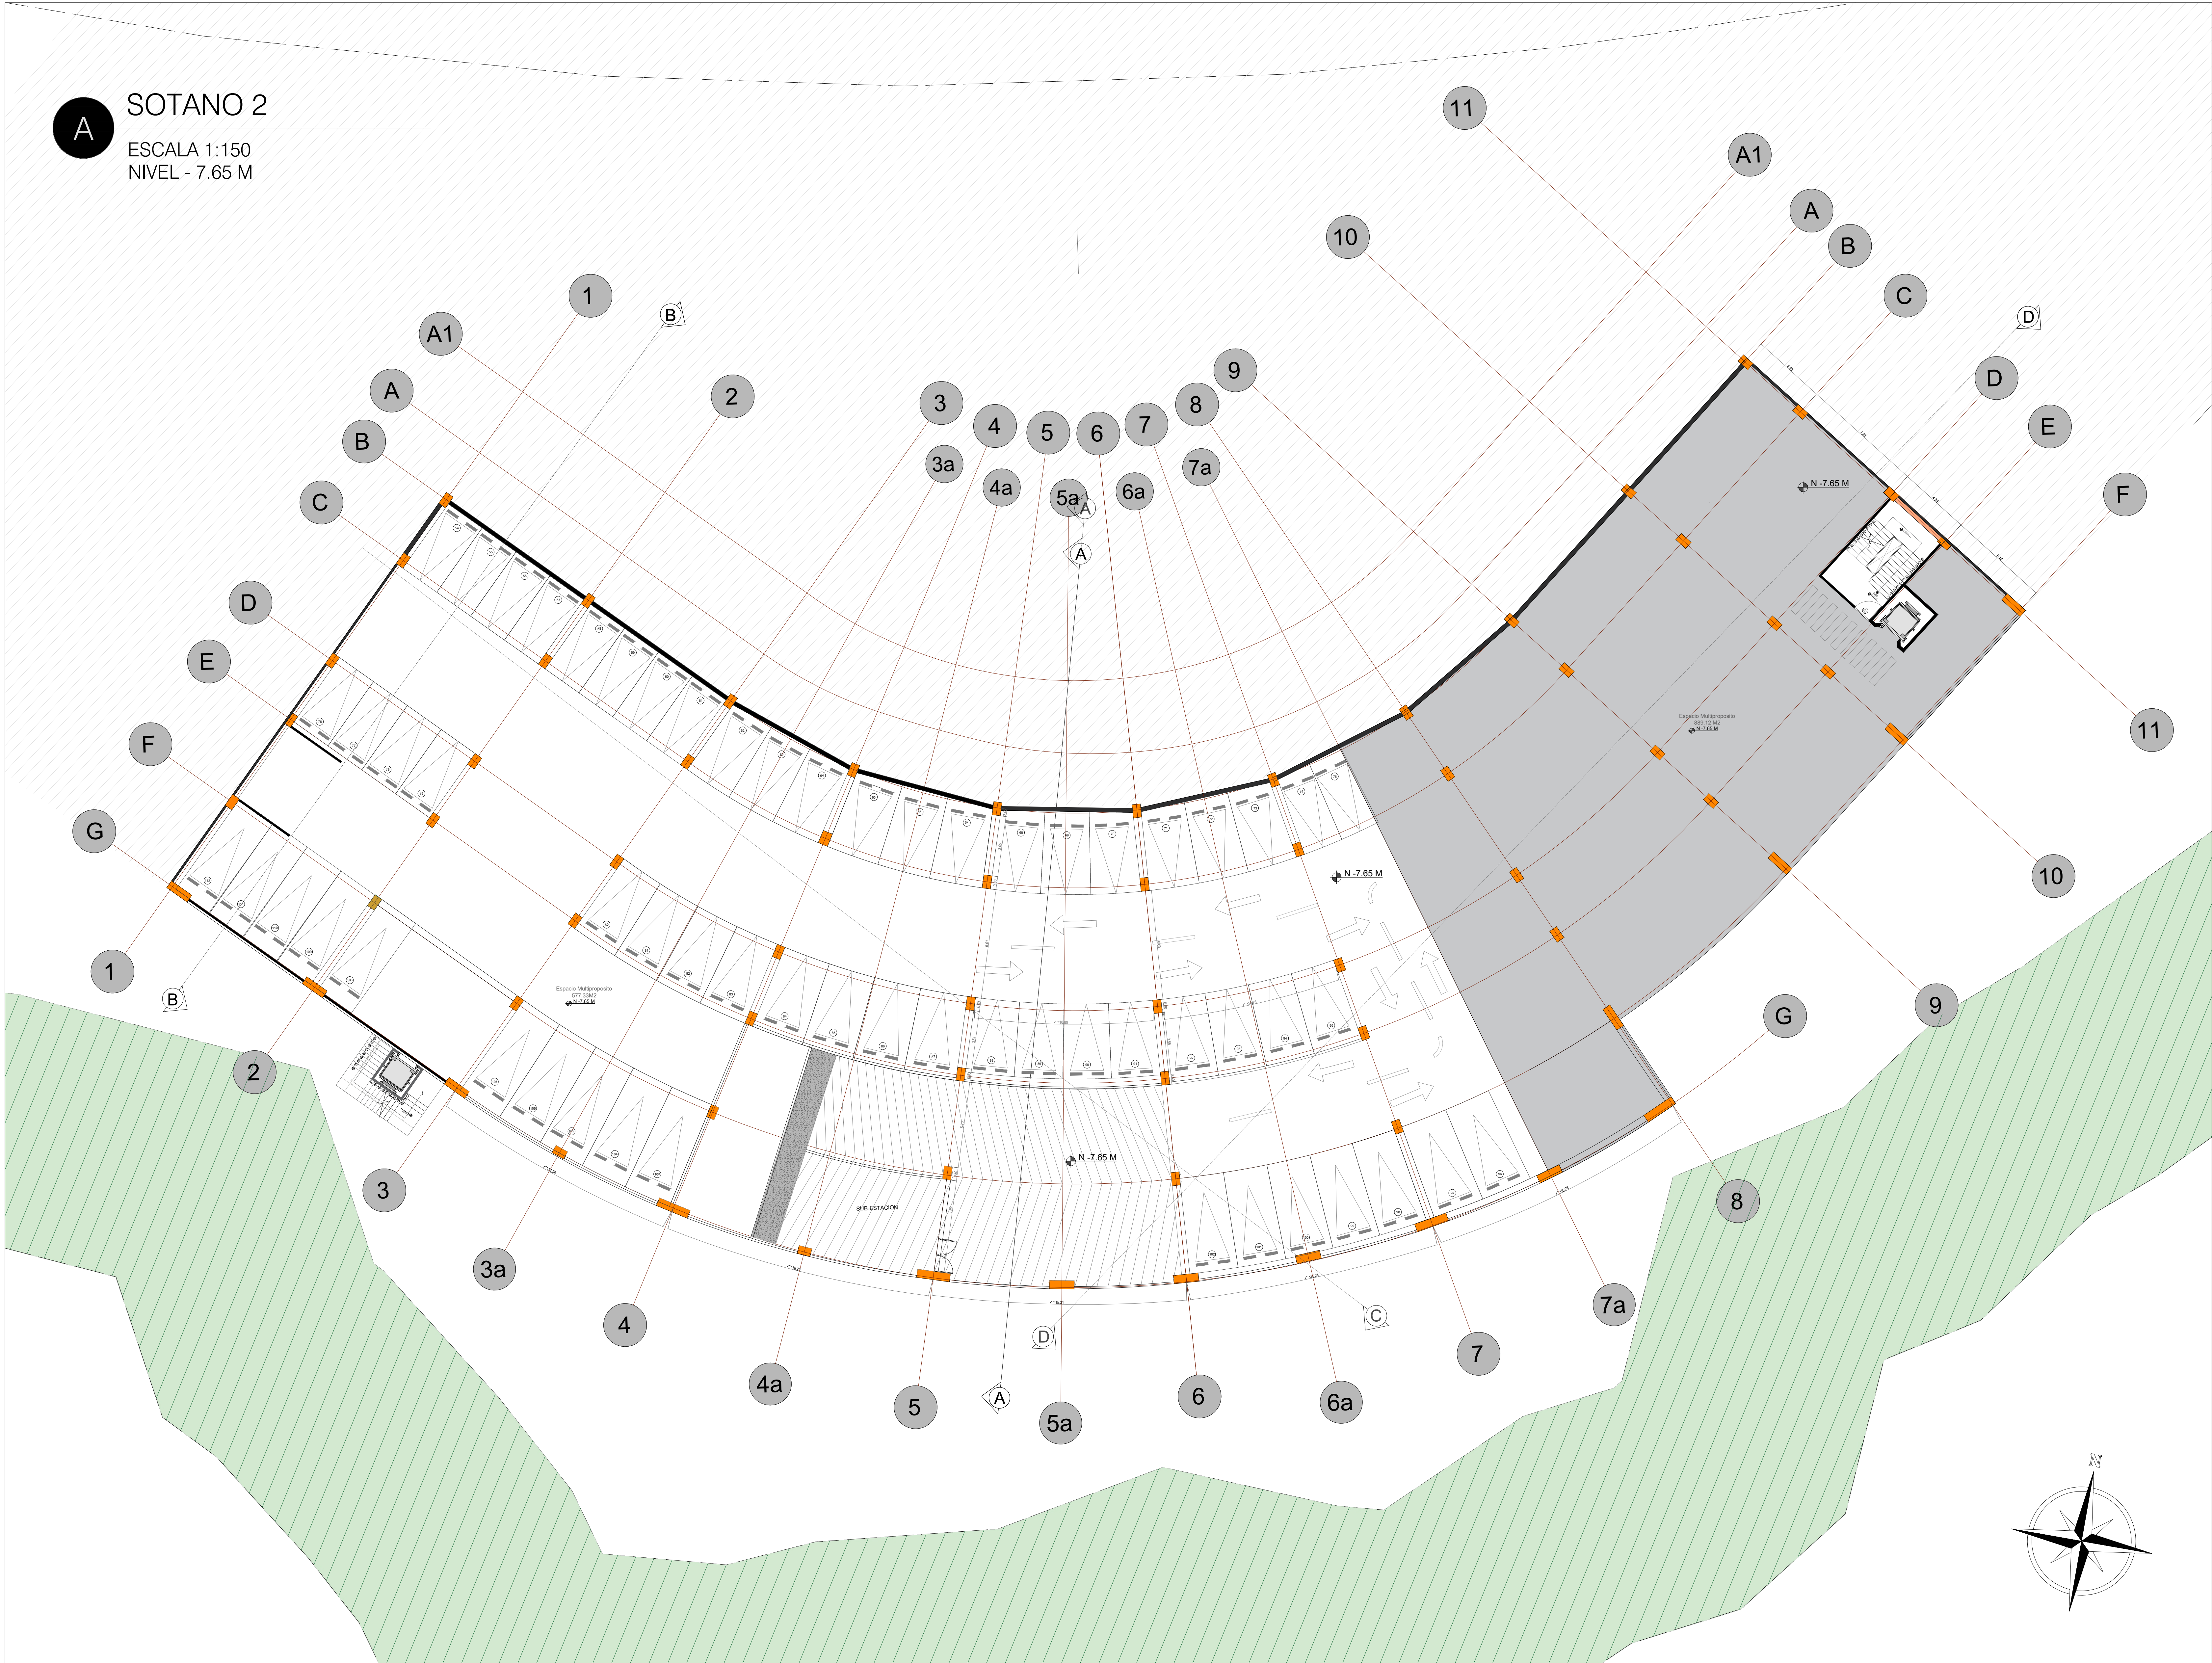

**A** SOTANO 2  
ESCALA 1:150  
NIVEL - 7.65 M

PLANO PA\_A 04 20

BAHÍA GUACAMAYAS  
PROYECTO COMERCIAL

PROYECTO:

**BAHÍA GUACAMAYAS**  
"UN DESARROLLO EXCEPCIONAL"

DISEÑO Y CONSTRUYE:

**Numancia**

DEPARTAMENTO DE RISARALDA  
DIRECCIÓN:  
VEREDA FONDA CENTRAL LOTE 3.  
SECTOR CERRITOS, PEREIRA

DR. RODRIGO OCAMPO OSSA  
C.C: 19101474  
GERENTE DEL PROYECTO

JULIAN DAVID ZAPATA  
T.P. A17863017-1090149794  
DIRECTOR DE OBRA

CONTENIDO:  
Planta Arquitectónica N.E.-3.65mts  
Sótano 1.

TRAMITE:  
Licencia de Construcción  
Modificación

EQUIPO DE TRABAJO

MELISA GIRALDO OSORIO  
ARQUITECTA  
M.P. A178212020-1088030422

NOMBRE DEL ARCHIVO:  
16072025\_Plantas Bahía Guacamayas.dwg

FECHA:  
Mod\_Junio\_2025

ESCALA:  
INDICADAS

VERSIÓN DEL ARCHIVO | 02

ANOTACIONES:  
Mod\_Junio\_2025 - ANOTACIONES

**Nota:**  
El contenido de este documento es confidencial y dirigido únicamente a su destinatario (s) queda expresamente prohibida su reproducción y divulgación de manera total o parcial sin autorización Todos los derechos reservados.

BAHÍA GUACAMAYAS  
PROYECTO COMERCIAL

PLANO PA\_A 04 20