


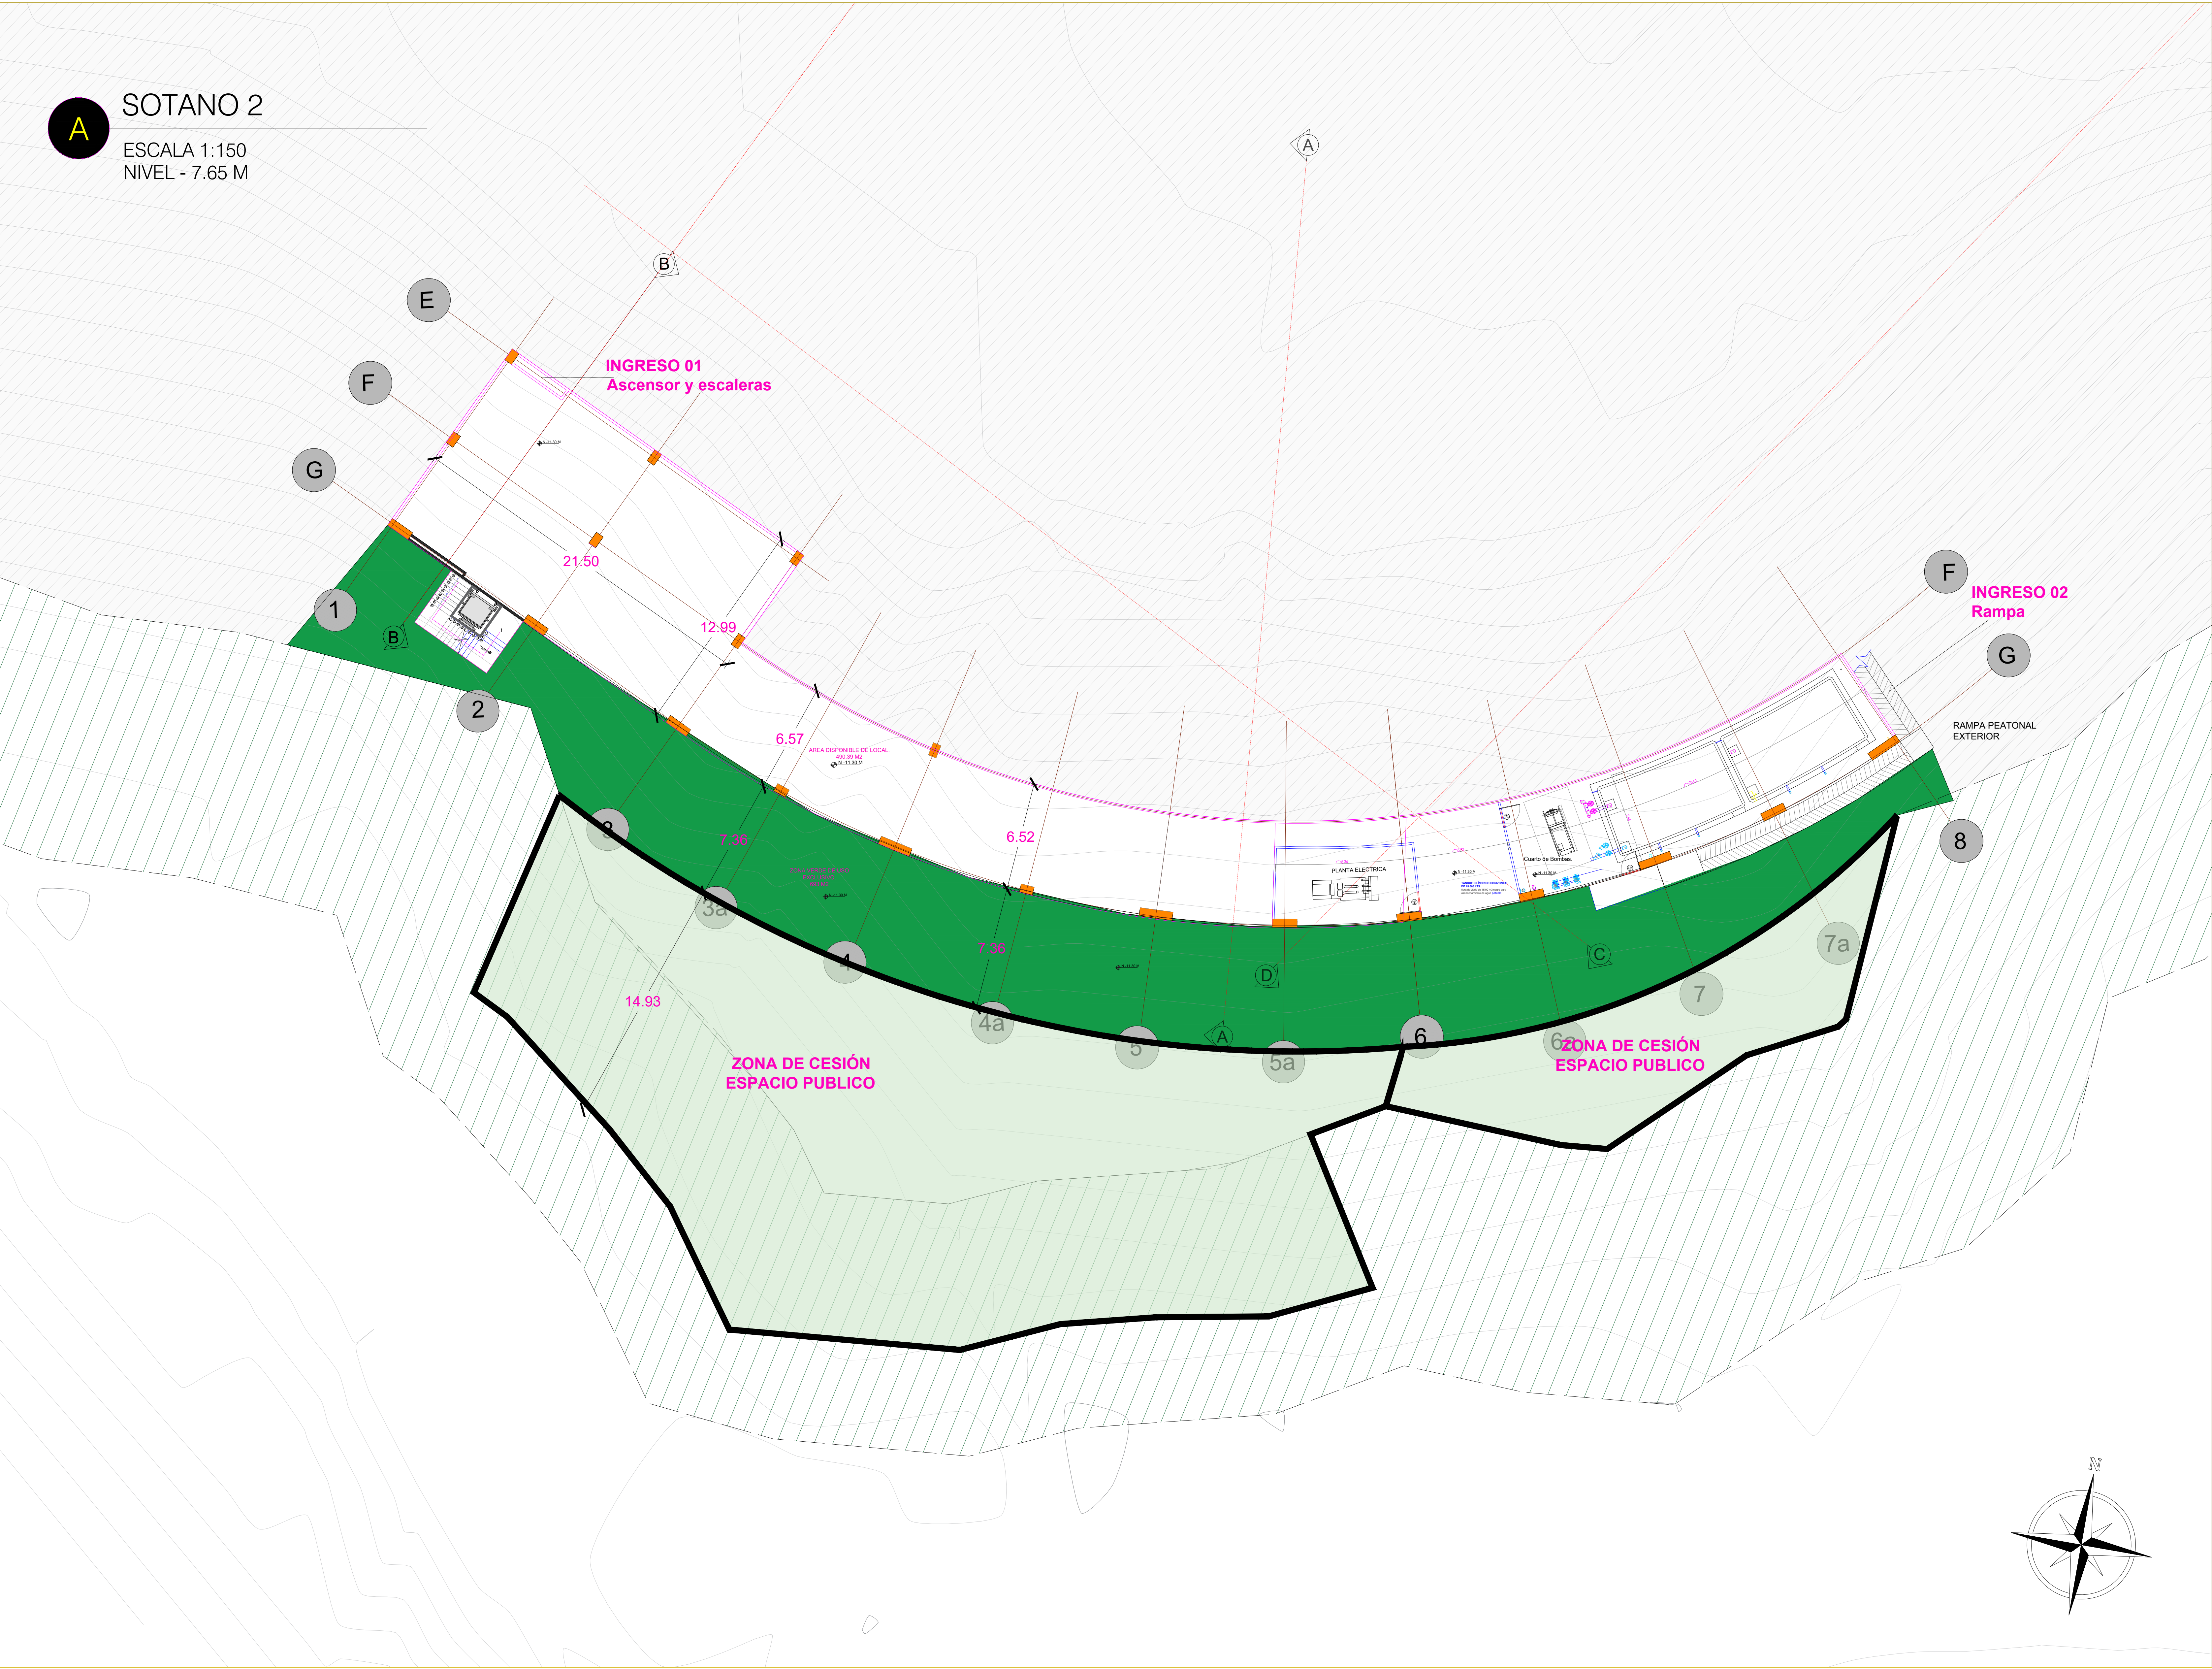

A

SOTANO 2

ESCALA 1:150
NIVEL - 7.65 M

PLANO PA_A 04 20

BAHÍA GUACAMAYAS
PROYECTO COMERCIAL

PROYECTO:

BAHÍA GUACAMAYAS
"UN DESARROLLO EXCEPCIONAL"

DISEÑO Y CONSTRUYE:

Numancia

DEPARTAMENTO DE RISARALDA
DIRECCIÓN:
VEREDA FONDA CENTRAL LOTE 3.
SECTOR CERRITOS, PEREIRA

DR. RODRIGO OCAMPO OSSA
C.C. 19101474
GERENTE DEL PROYECTO

JULIAN DAVID ZAPATA
T.P. A17863017-1090149794
DIRECTOR DE OBRA

CONTENIDO:
Planta Arquitectónica N.E.-3.65mts
Sótano 3.

TRAMITE:
Licencia de Construcción
Modificación

EQUIPO DE TRABAJO

MELISA GIRALDO OSORIO
ARQUITECTA
M.P. A178212020-1088030422

NOMBRE DEL ARCHIVO:
16072025_Plantas Bahía Guacamayas.dwg

FECHA:
Mod_Junio_2025

ESCALA:
INDICADAS

VERSIÓN DEL ARCHIVO | 02

ANOTACIONES:
Mod_Junio_2025 - ANOTACIONES

.....

.....

.....

.....

Nota:

El contenido de este documento es confidencial y dirigido únicamente a su destinatario (s) queda expresamente prohibida su reproducción y divulgación de manera total o parcial sin autorización Todos los derechos reservados.

BAHÍA GUACAMAYAS
PROYECTO COMERCIAL

PLANO PA_A 04 20